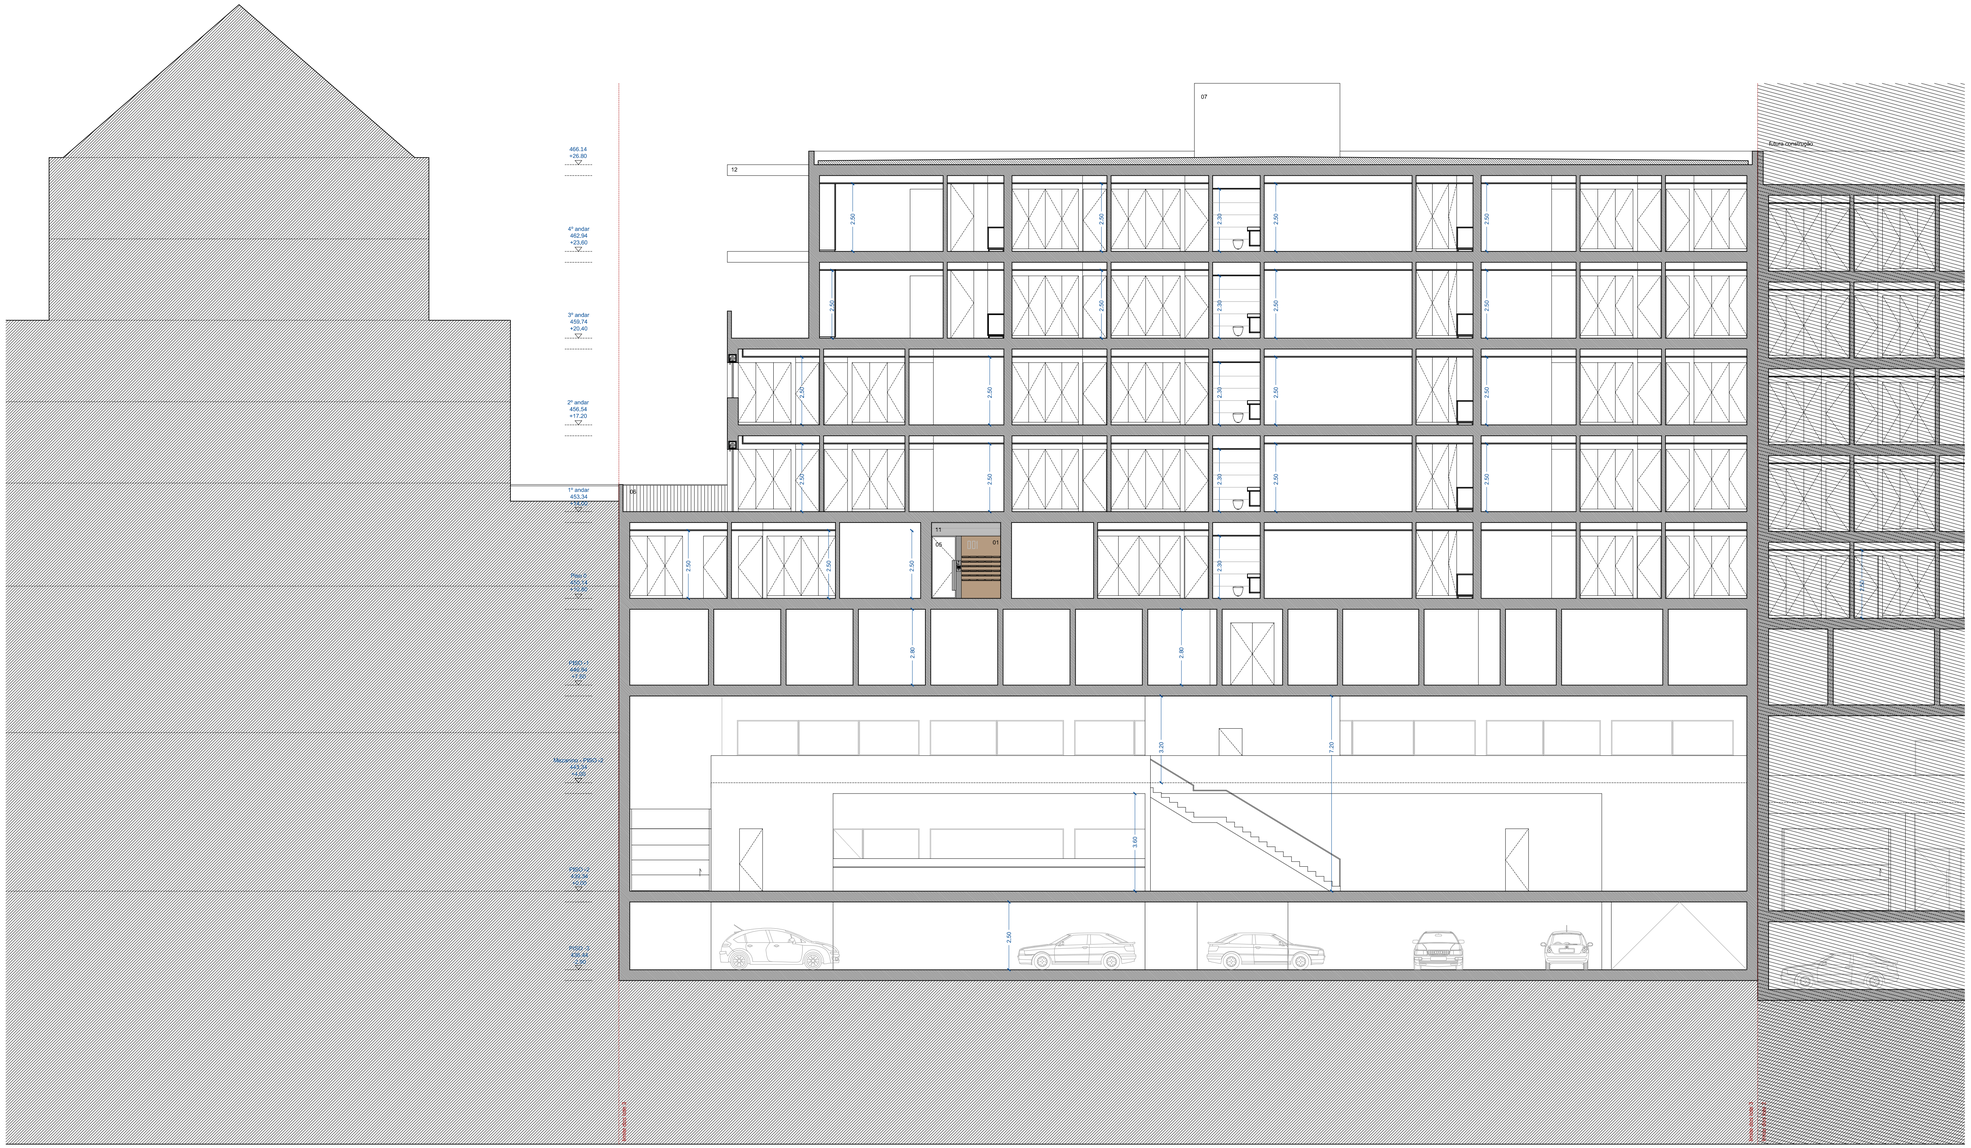


CORTE C2
cota base 439m

LEGENDA de MATERIAIS EXTERIORES de ACABAMENTO

01 PAINÉIS DE TRESPA METEON REF.: NW05 LOFT BROWN
02 FACHADA VENTILADA COM PAINÉIS CERÂMICOS DEKTON MARINA
03 FACHADA VENTILADA COM PAINÉIS CERÂMICOS DEKTON VADI GRAFITE
04 RIPAS EM ALUMÍNIO A IMITAR MADEIRA
05 CAIXILHARIA RPT EM ALUMÍNIO LACADO À COR CINZA ANTRACITE RAL 7016
06 GUARDAS EM FERRO LACADO À COR E ACABAMENTO DA CAIXILHARIA
07 REBOCO AREADO FINO PINTADO COM TINTA PLÁSTICA BRANCA (muros)
08 VIDRO DUPLO INCOLOR
09 CHAPA LISA DE ALUMÍNIO LACADA À COR DA CAIXILHARIA
10 PORTÃO SECCIONADO LACADO À COR CINZA ANTRACITE RAL 7016
11 LÂMINAS VENEZIANAS COM MOLDURA E FIXAÇÃO OCULTA EM ALUMÍNIO À COR E ACABAMENTO DA CAIXILHARIA
12 BETÃO PREPARADO PARA FICAR A VISTA
13 PAINEL SOLAR

blk porto arquitectura

DISCURSURBANO, LDA 2309

EDIFÍCIO DE HABITAÇÃO COLETIVA
Rua Jaime Campos - VILA REAL
Lote 3 - Alvará 1/92

COMUNICAÇÃO PRÉVIA _ Projeto de Arquitetura
setembro 2024

CORTE C2
esc. 1/100

13

R. Altino Coelho, 478. 4470-180 MAIA _tel.+351 229488776 _geral@blk-porto.pt _www.blk-porto.pt