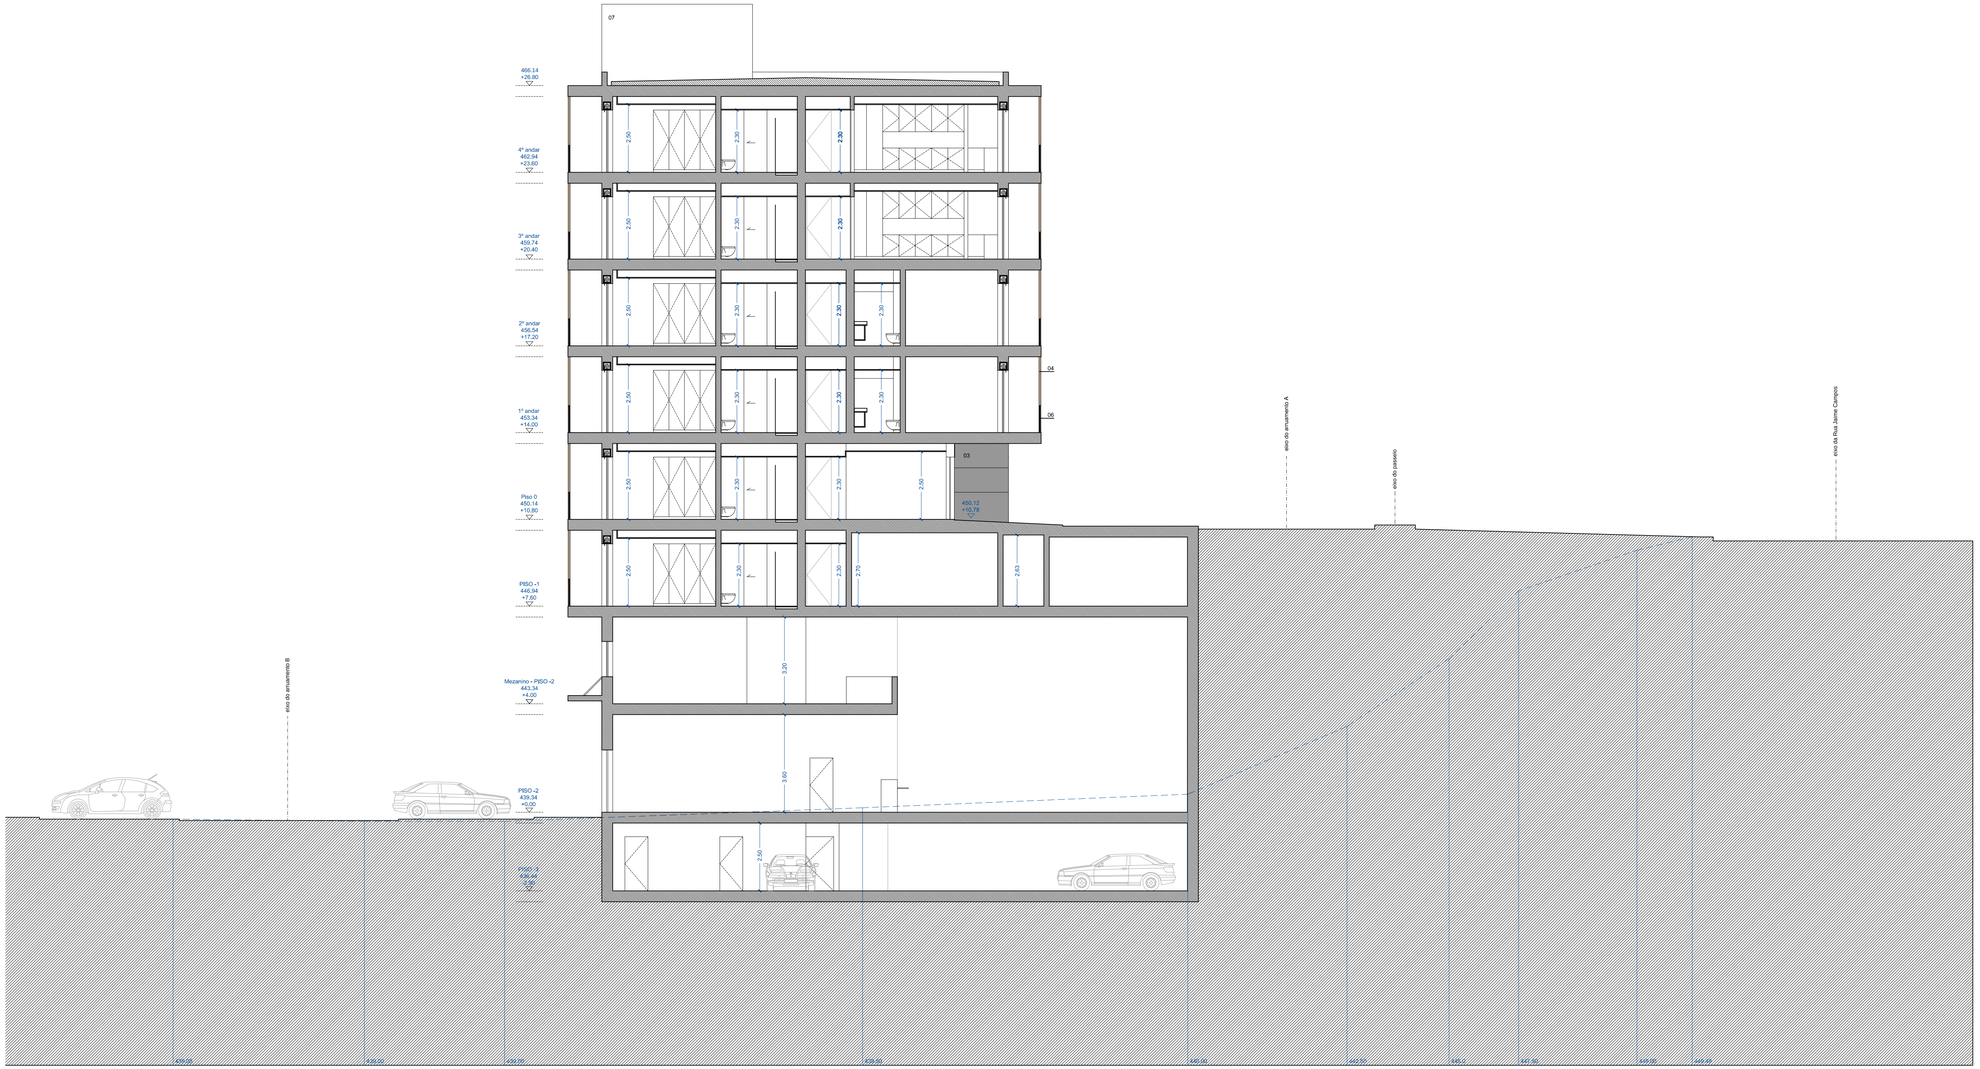

CORTE C3
cota base 430m

LEGENDA de MATERIAIS EXTERIORES de ACABAMENTO

01 PAINÉIS DE TRESPA METEON REF. NW05 LOFT BROWN
02 FACHADA VENTILADA COM PAINÉIS CERÂMICOS DEKTON MARINA
03 FACHADA VENTILADA COM PAINÉIS CERÂMICOS DEKTON VIOH GRAFITE
04 RIPAS EM ALUMÍNIO A IMITAR MADEIRA
05 CAIXILHARIA RPT EM ALUMÍNIO LACADO À COR CINZA ANTRACITE RAL 7016
06 GUARDAS EM FERRO LACADO À COR E ACABAMENTO DA CAIXILHARIA
07 REBOCO AREADO FINO PINTADO COM TINTA PLÁSTICA BRANCA (muros)
08 VIDRO DUPLO INCOLOR
09 CHAPA LISA DE ALUMÍNIO LACADA À COR DA CAIXILHARIA
10 PORTÃO SECCIONADO LACADO À COR CINZA ANTRACITE RAL 7016
11 LÂMINAS VENEZIANAS COM MOLDURA E FIXAÇÃO OCULTA EM ALUMÍNIO À COR E ACABAMENTO DA CAIXILHARIA
12 BETÃO PREPARADO PARA FICAR À VISTA
13 PAINEL SOLAR

DISCURSURBANO, LDA 2309

EDIFÍCIO DE HABITAÇÃO COLETIVA
Rua Jaime Campos - VILA REAL
Lote 3 - Alvará 1/92

COMUNICAÇÃO PRÉVIA _ Projeto de Arquitetura
setembro 2024

CORTE C3
esc. 1/100

14

R. Altino Coelho, 478. 4470-180 MAIA _tel.+351 229488736 _geral@blk-porto.pt _www.blk-porto.pt